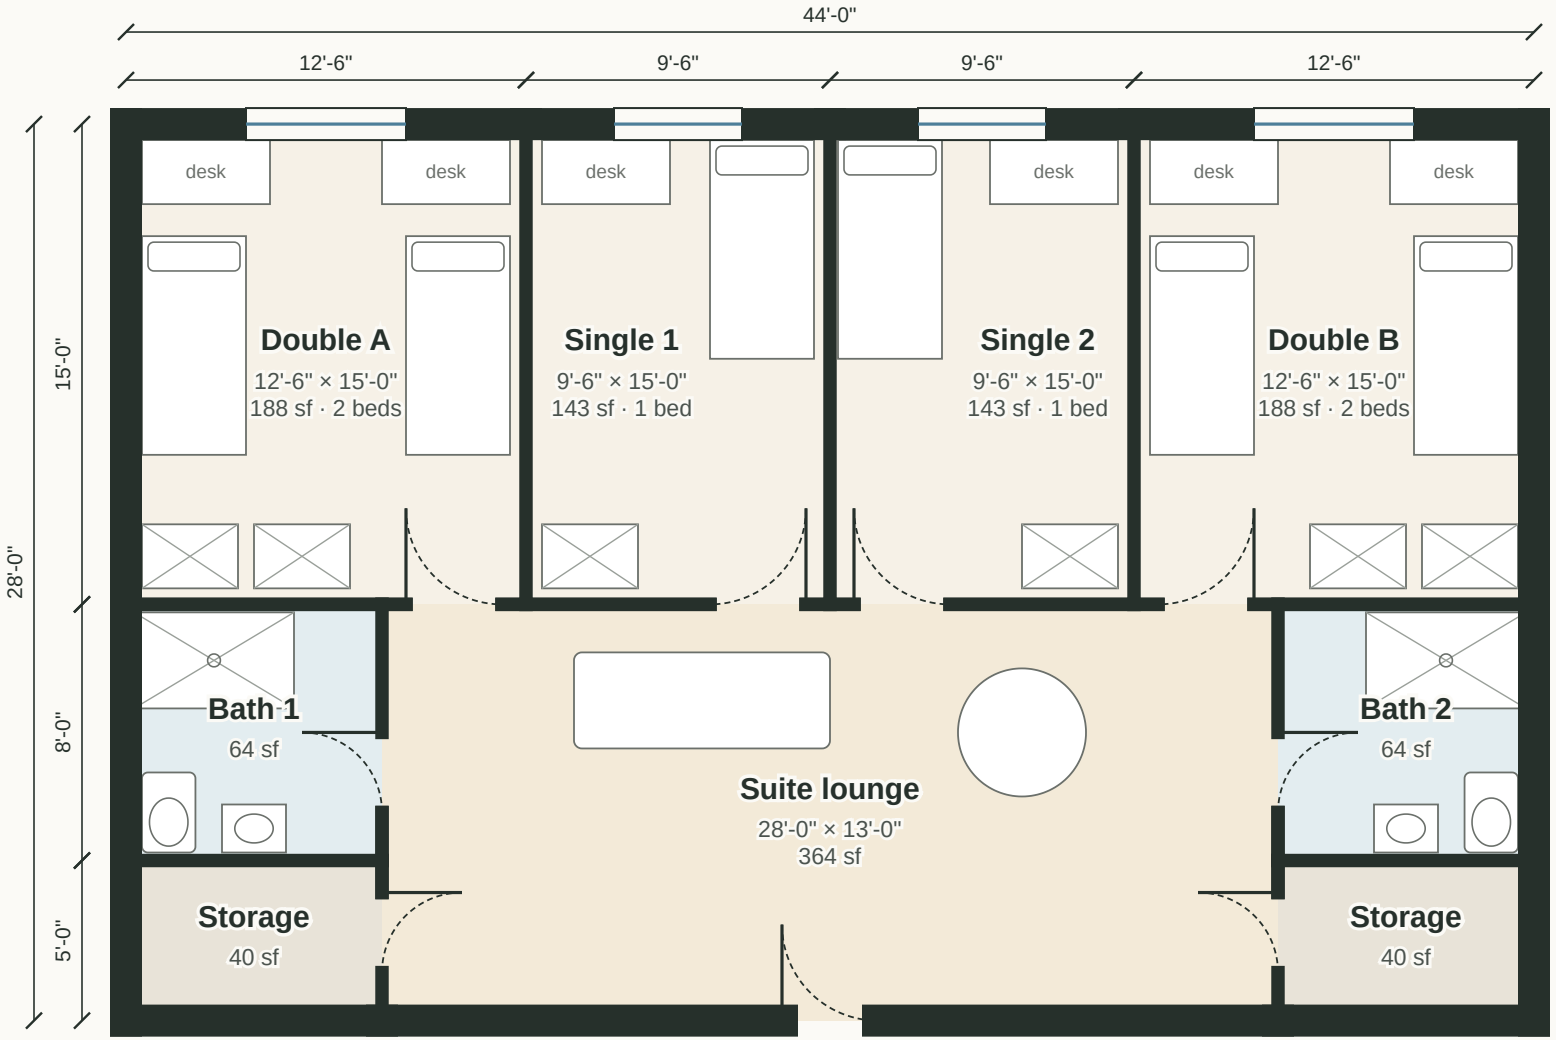


Trinity Peaks · Six-person suite

Two doubles + two singles + suite lounge, no triples

6 beds · envelope 44'-0" × 28'-0" = 1,232 sf · 205.3 sf per bed

0 5 10 ft

graphic scale of assumed dimensions

SCHEMATIC EXPLORATION · v1 · 2026-11-06 · Dimensions are exploratory assumptions (studies/assumptions.json), not measurements.

Not code-reviewed, not an accessibility determination, not for construction. Orientation not established (no north arrow).

Independent student design study by Ivan Minier, drawn with AI assistance. Not a UVM design or an adopted part of the Trinity Redistricting proposal.